




1/2 DOORSNEDE A-A

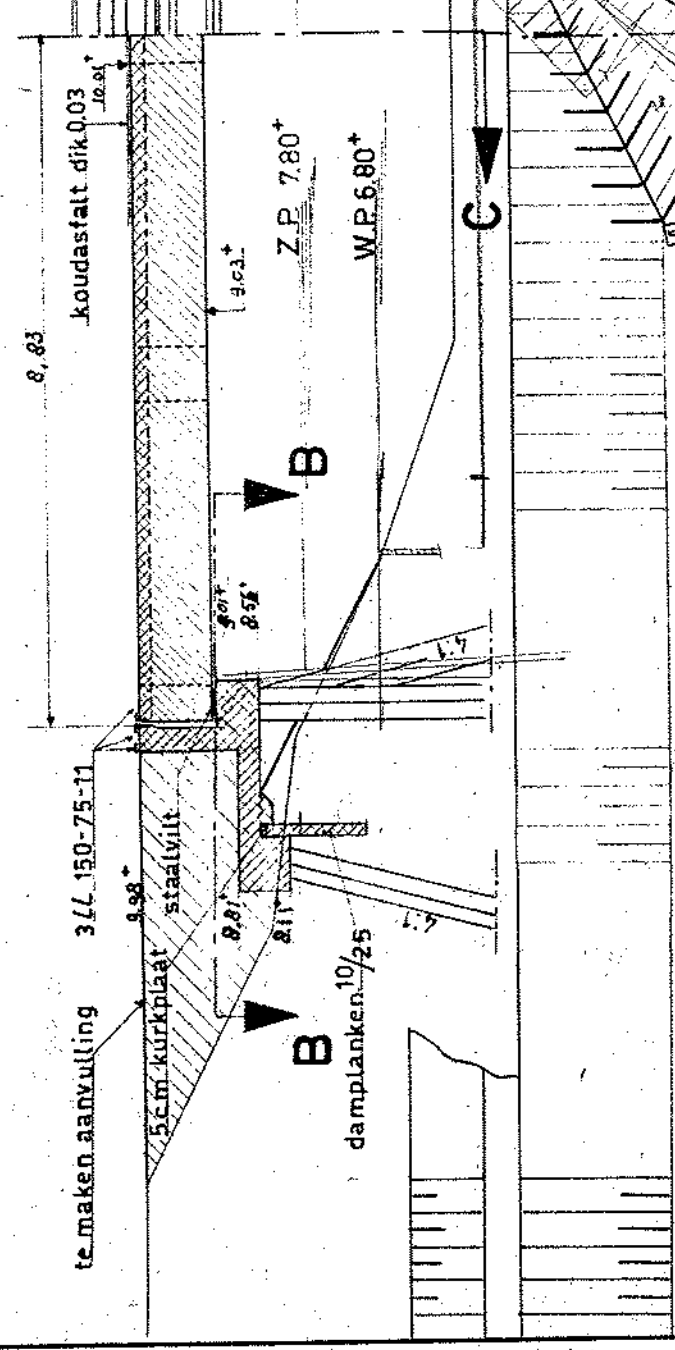


1/2 AANZICHT

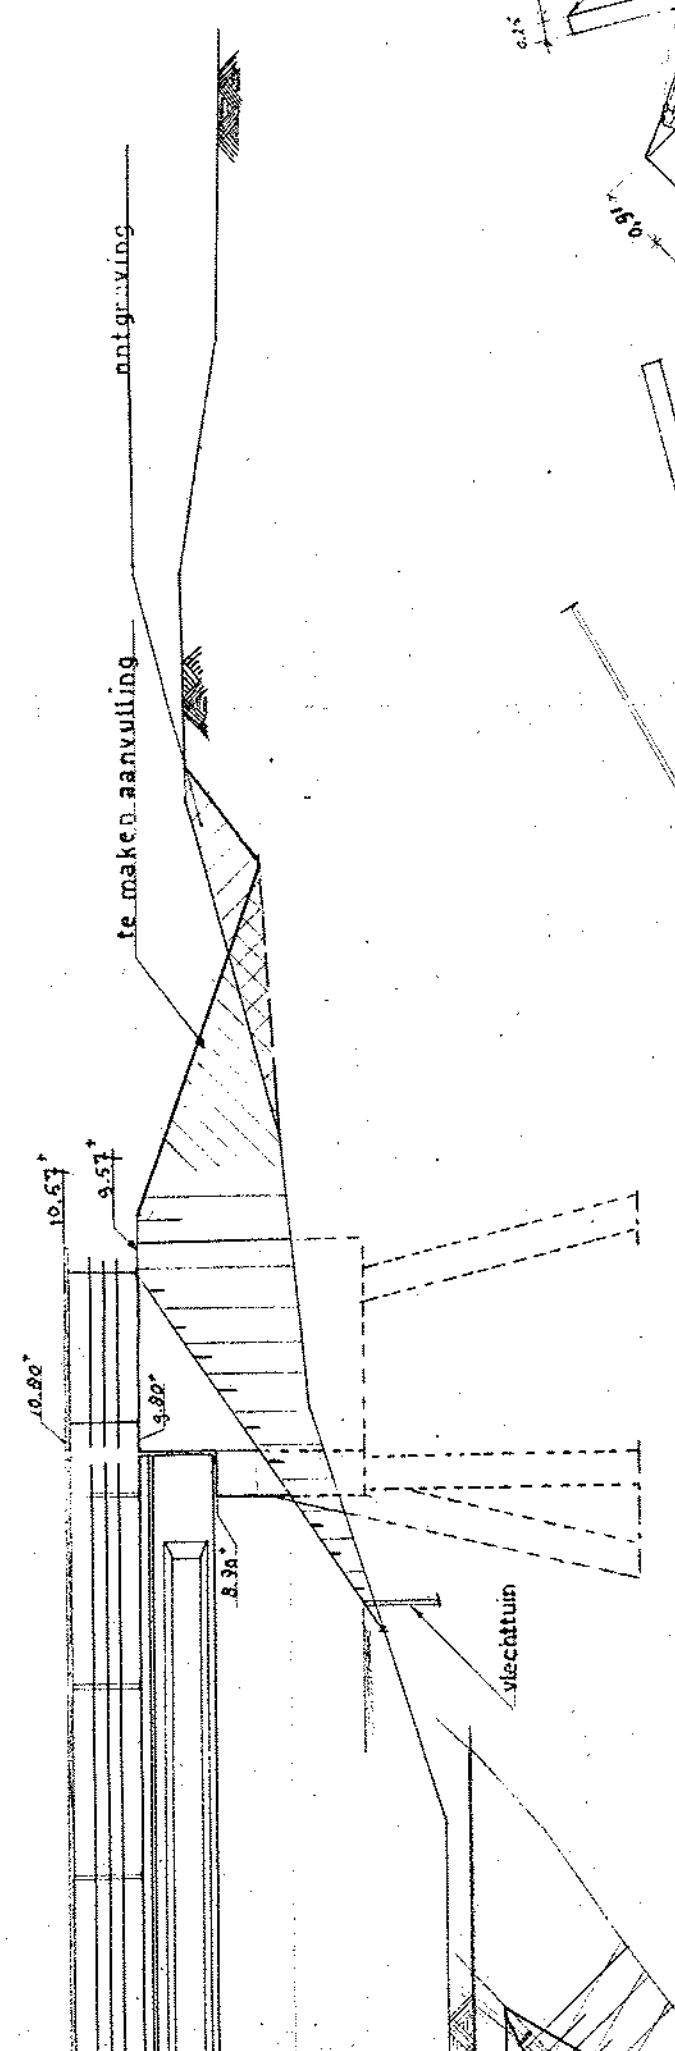


BOVENAANZICHT

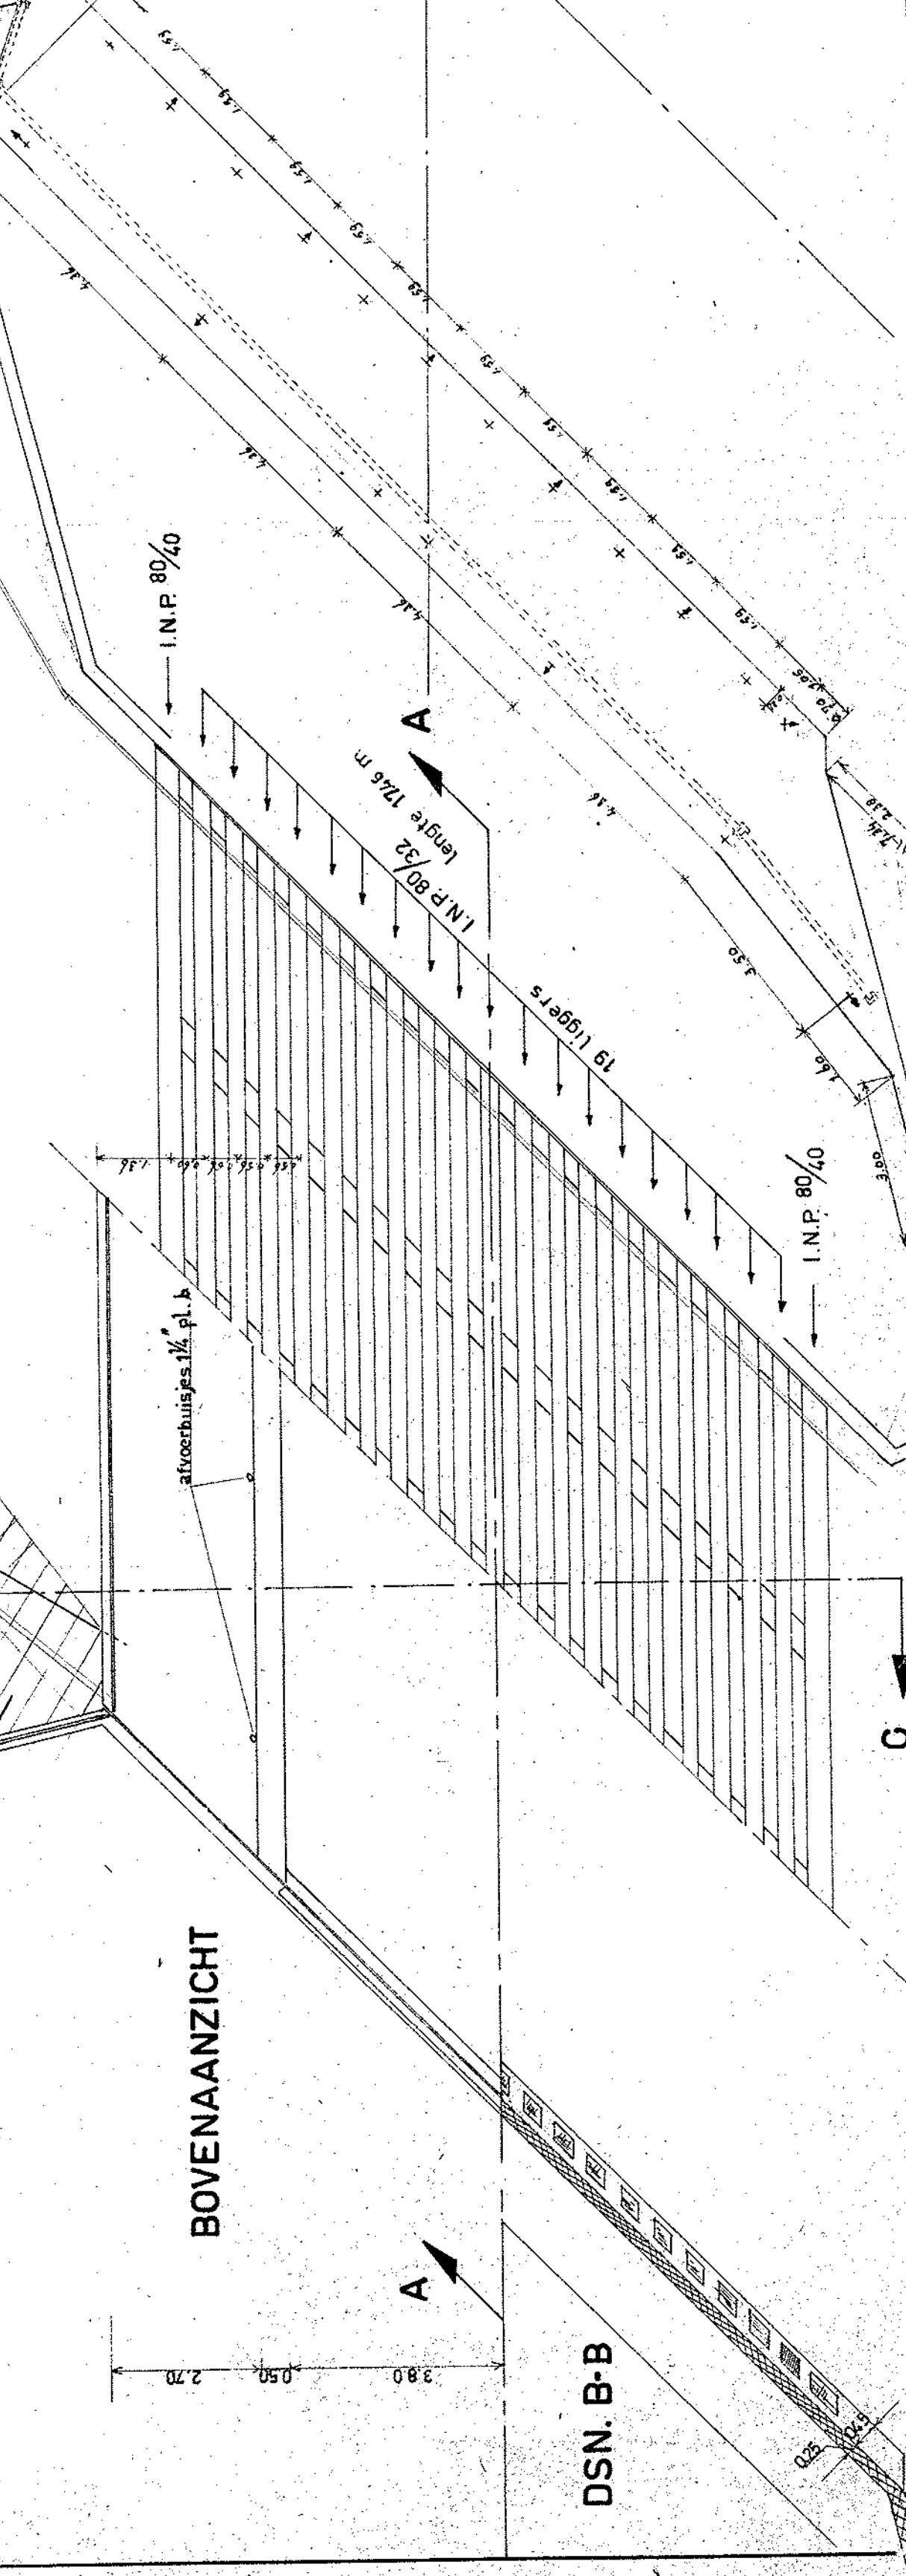


DSN. B-B

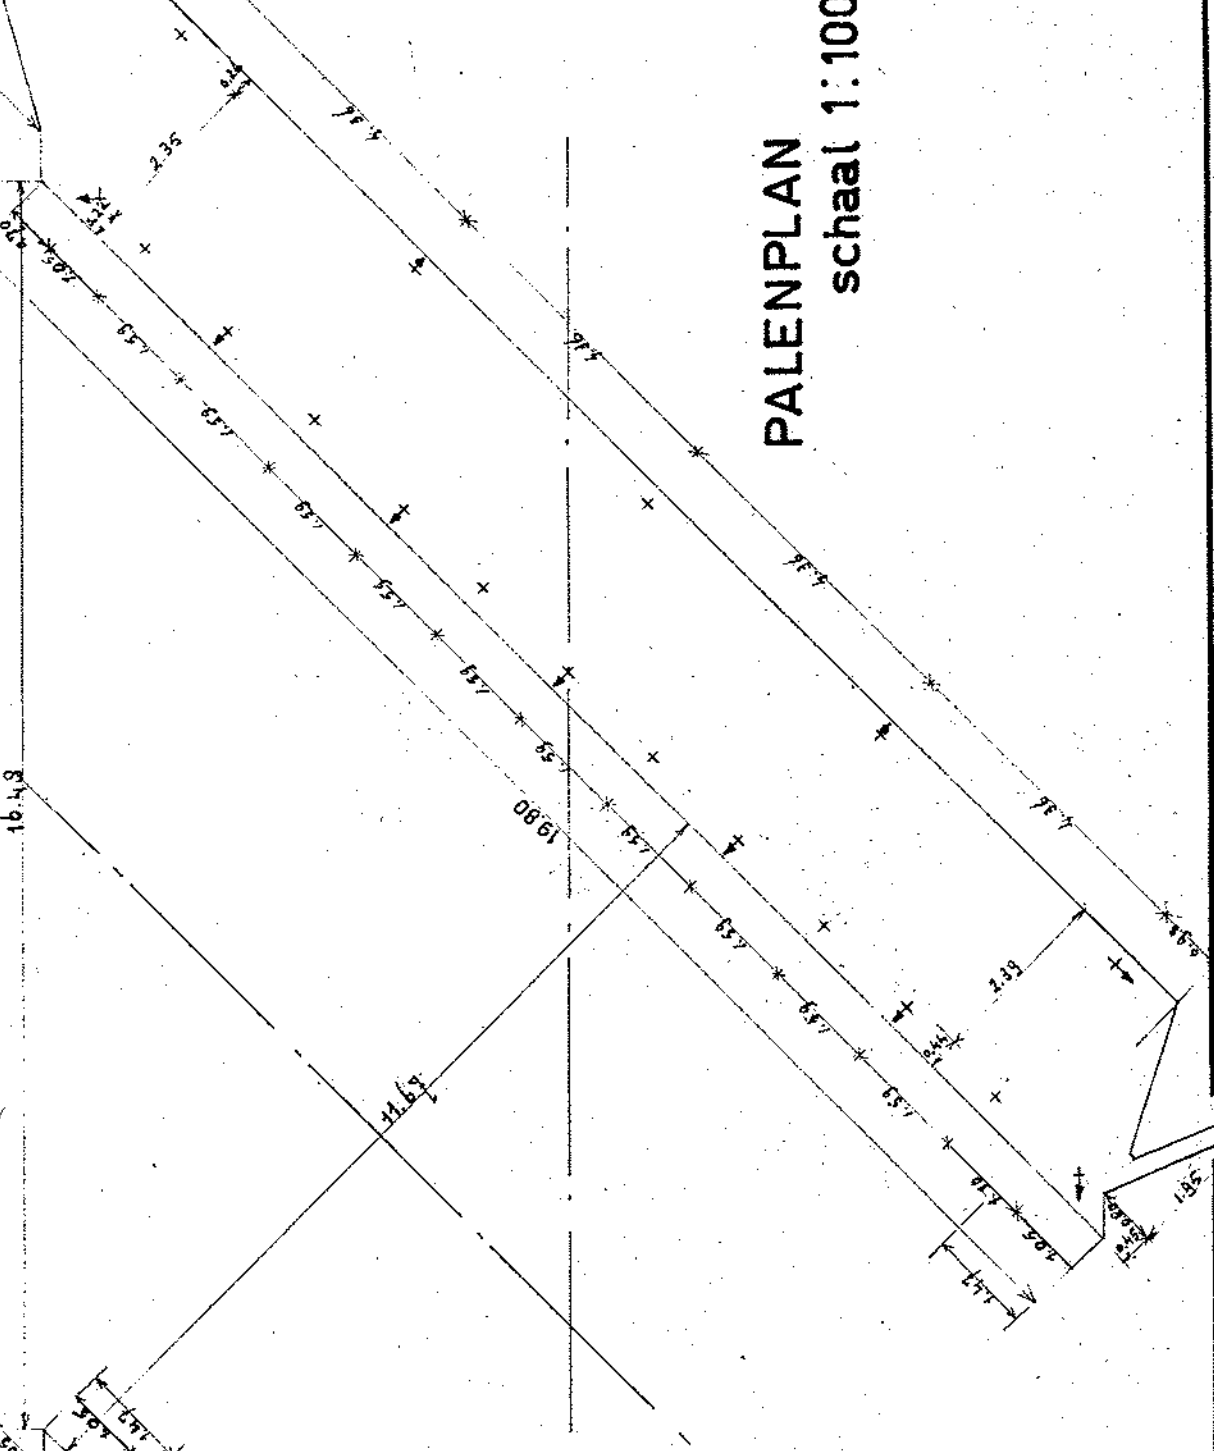

PALENPLAN  
schaal 1:100

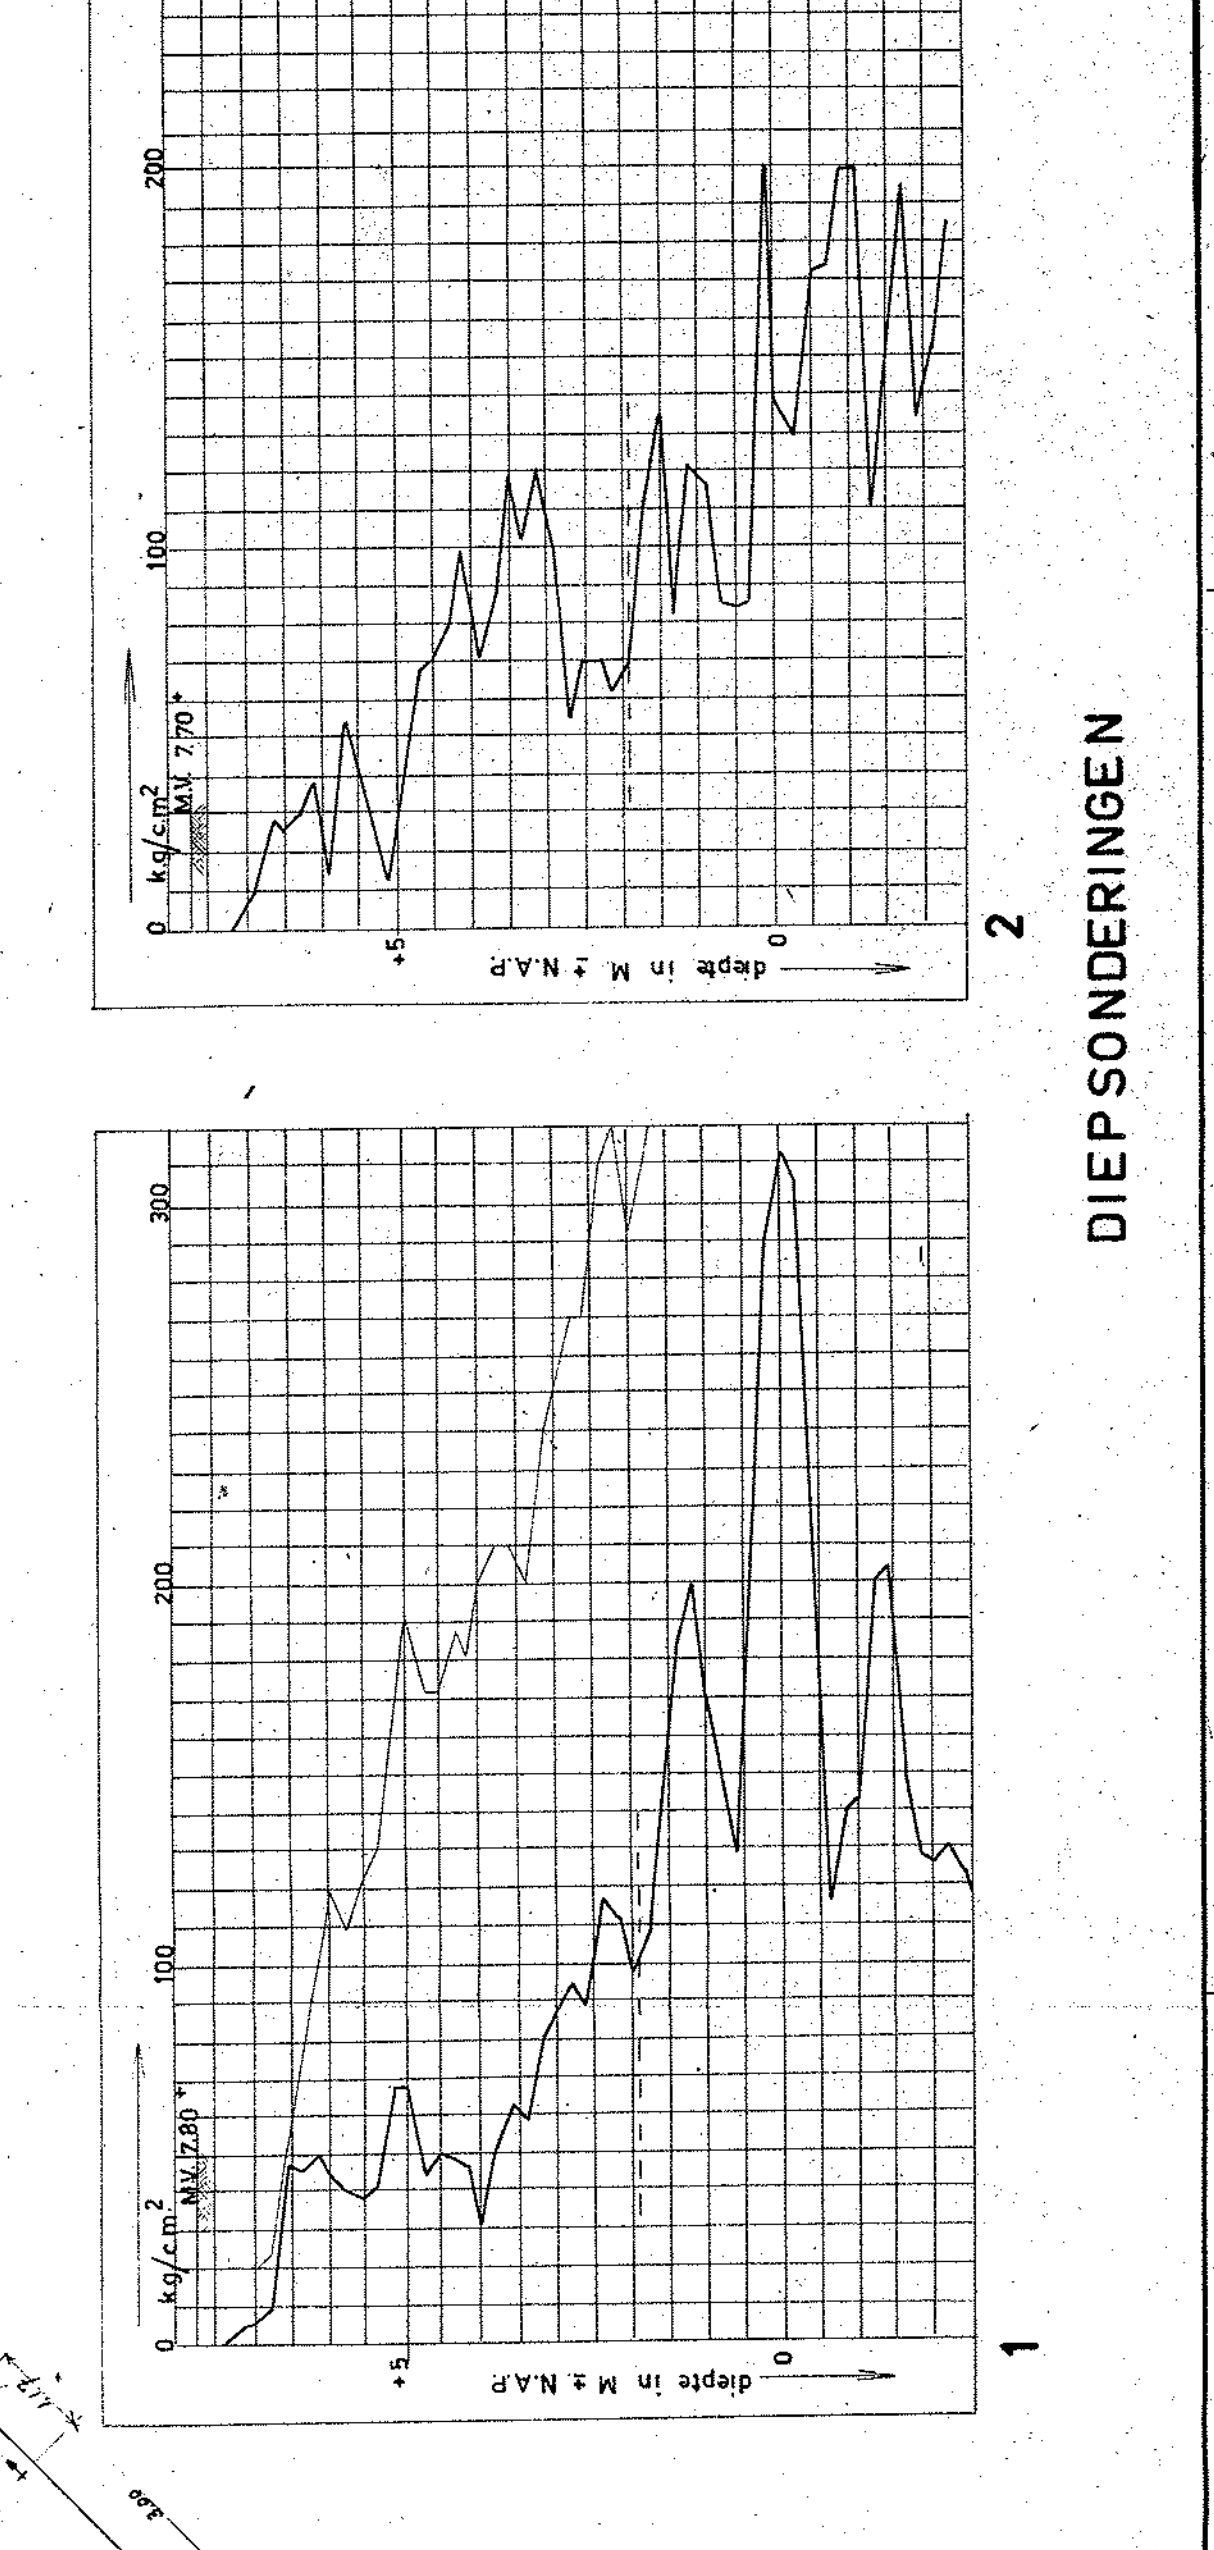

2

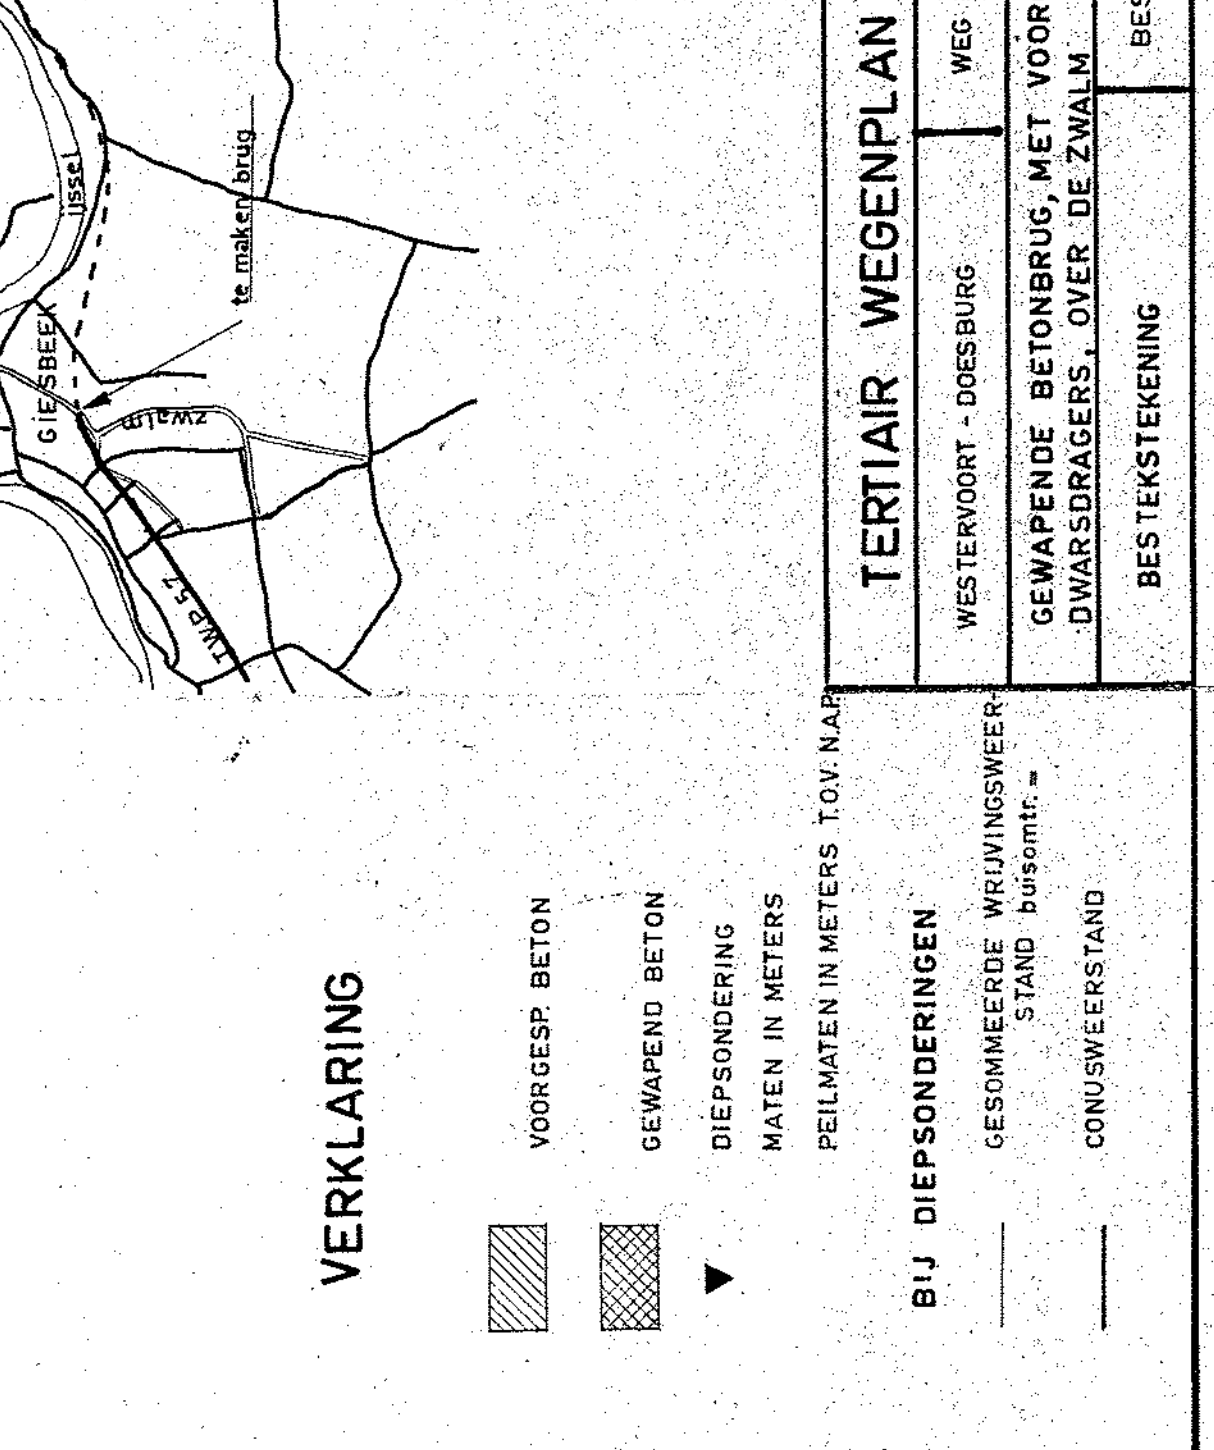


VERKLARING

- VOORGESP. BETON
- GEWAPEND BETON
- DIEPSONDERING
- MATEN IN METERS
- PEILMATEN IN METERS TOV. N.A.P.

BIJ DIEPSONDERINGEN  
GESOMMEERDE WRIJWINGSWEER-  
STAND busmtr. =  
CONUSWEERSTAND

SITUATIE SCHAAL 1:50.000

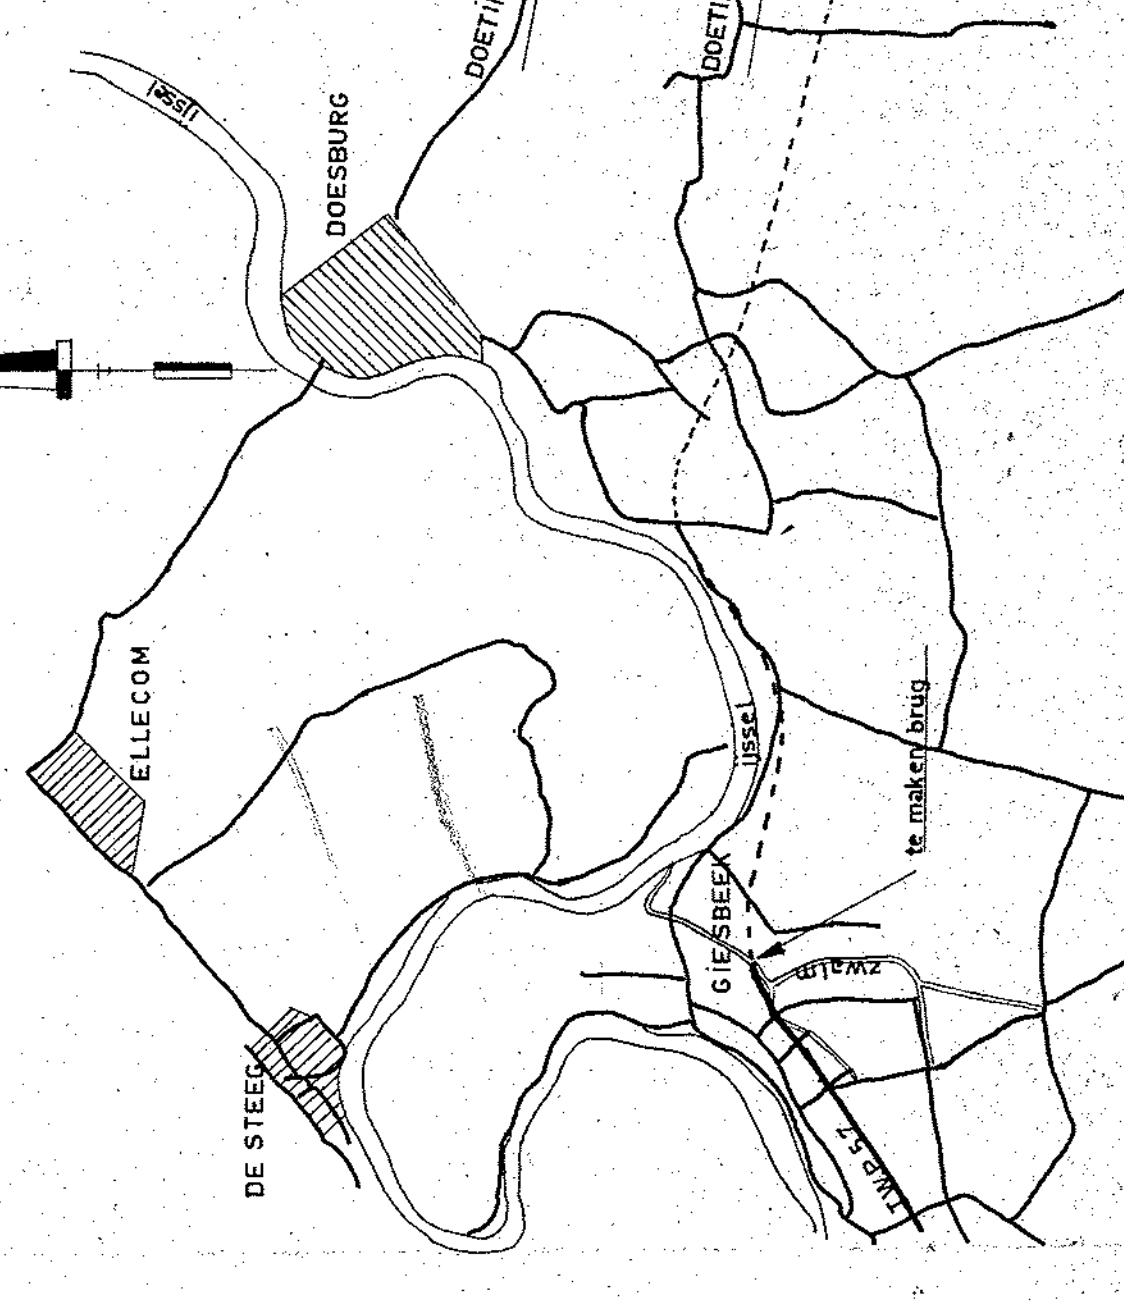

| TERTIAIR WEGENPLAN VAN GELDERLAND                                                |                  |      |      |
|----------------------------------------------------------------------------------|------------------|------|------|
| WEG N° 57                                                                        | GEMEENTE ANGERLO |      |      |
| GEWAPENDE BETONBRUG, MET VOORGESPANNEN LANGS - EN<br>DWARSDRAGERS, OVER DE ZWALM |                  |      |      |
| BESTEK N° T. 27                                                                  | BLAD 1           | GEZ. | GEZ. |

SITUATIE SCHAAL 1:1000

gem. Angerlo

